



CONCEPT, NOT FOR FABRICATION

ZeerBox · github.com/BoujeeEnjinia1701/zeerbox

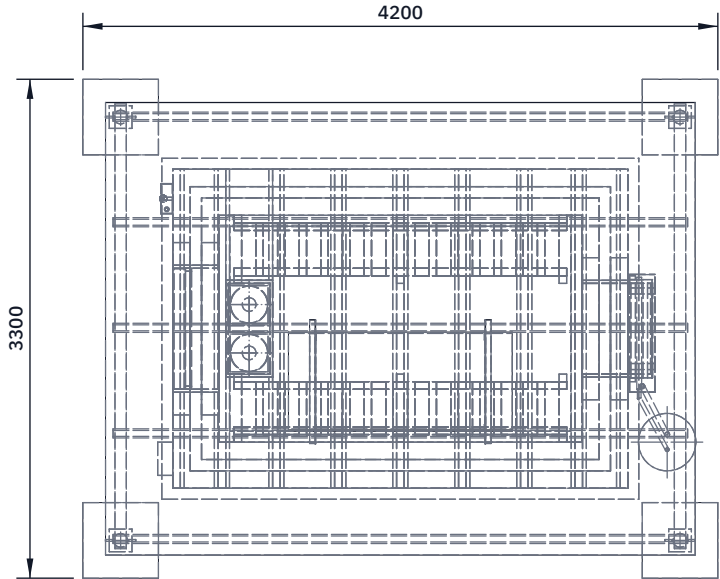


TOP VIEW

Scale 1:50; looking down (along -Z)

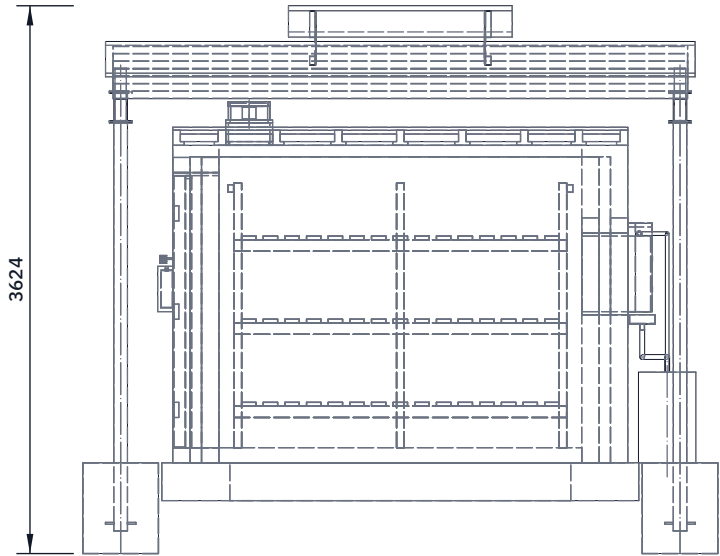

FRONT VIEW


Scale 1:50; looking at the front (along +Y)

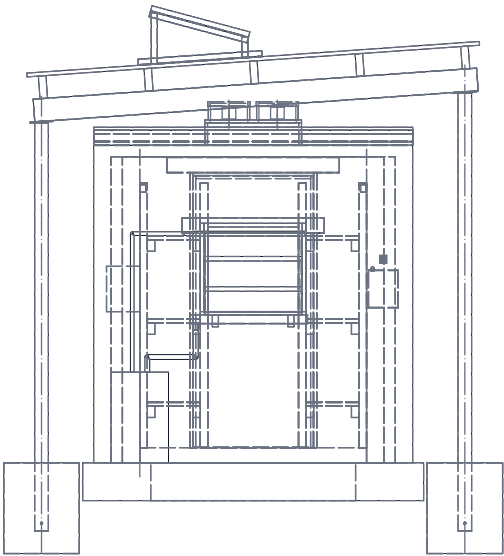

RIGHT VIEW

Scale 1:50; looking at the right side (along -X)

REV	DESCRIPTION	DATE	BY
P1	Preliminary GA from the TRL 3 model (ZBX-CAL-001)	2026-09-25	AC
P2	150 mm pad; dry rice husk cavity fill; R3 80 % (DDR-002)	2026-09-25	AC
P3	Footings, lintels, framed ceiling and roof, ceiling fans (DDR-003)	2026-10-02	AC
P4	Controller mode lamp; six-plate sensor shield (DEC-001)	2026-10-02	AC

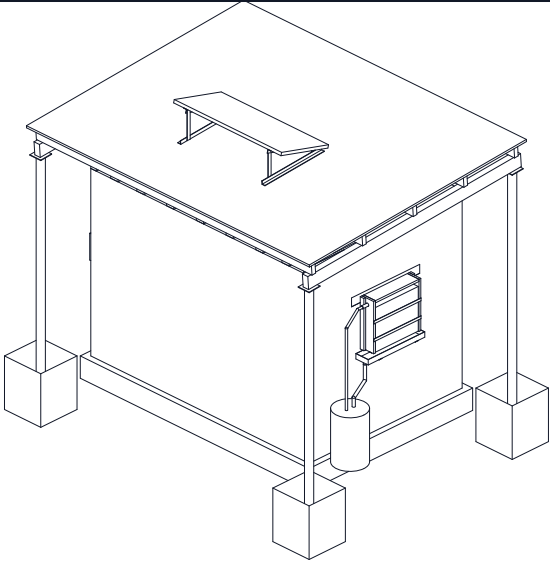

ISOMETRIC VIEW

Not to scale; crates hidden; seen from the front right and above, about 30 deg elevation

KEY DIMENSIONS (MM) AND DATA

Overall 4200 x 3300 x 3624 H (roof, posts, sump, panel)

Room 2400 x 1500 x 2000 H inside; 7.2 m3

Walls 115 + 75 dry rice husk + 115 = 305; outside 3010 x 2110

Strip footing 450 x 250; floor 100 brick on sand; wall top 2100

Ceiling: 50 x 100 joists, 50 insulation, 20 boards

Shade roof 3900 x 3000, 450 clear over ceiling, 4 deg

Beams 75 x 150, purlins 50 x 150; 4 posts 90 dia

Post footings 500 sq x 600 deep

Door 800 x 1800 clear, lined reveal, opens out, inside release

Pad 600 x 500 x 150, center 1250 above ground

2 fans 250 dia in a ceiling fan box, 1000 from the room center

Controller 80 x 200 x 250 clear lid, 22 mode lamp; 6-plate sensor shield

Racks 2200 x 450; shelves 300, 850, 1400 above floor

Aisle 600; 24 crates; 150 W panel 1480 x 670

Design day: store 24.3 °C, 10.7 K drop, about 560 m3/h (CAL-001)

At risk at TRL 3: R3 (store RH 81 %, 77 % unfavorable, vs 80 %)

PRELIMINARY, NOT FOR FABRICATION

ZEERBOX

github.com/BoujeeEnjinia1701/zeerbox

General arrangement, TRL 3 model

DRAWING NO. ZBX-DWG-001			REV P4	SHEET 1 of 1	SIZE ANSI B
SCALE 1:50	UNITS mm	PROJECTION 	DATE 2026-10-02	DRAWN Amish Chadha	

MATERIAL / NOTES Fired brick, dry rice husk fill, timber, corrugated steel; 12 V kit. See bom/bom.csv					
--	--	--	--	--	--