BUILD PLAN SKETCH, PLAN NOT YET BUILT

ZeerBox · github.com/BoujeeEnjinia1701/zeerbox

REV	DESCRIPTION	DATE	BY
P1	Making sketch for the prototype build plan	2026-10-02	AC

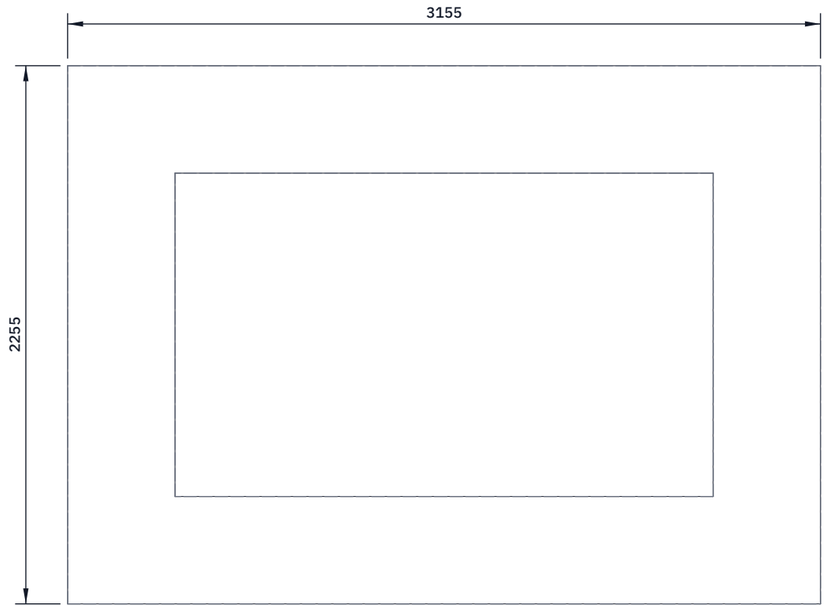

TOP VIEW

Scale 1:25; looking down (along -Z)

FRONT VIEW

Scale 1:25; looking at the front (along +Y)

RIGHT VIEW

Scale 1:25; looking at the right side (along -X)

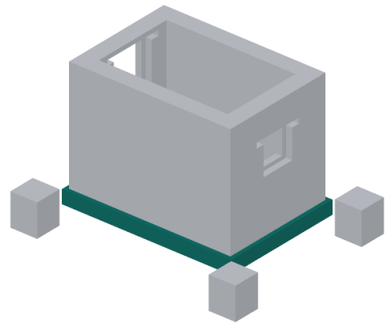

WHERE IT GOES

This part in colour, its neighbours in grey

HOW TO MAKE IT AND HOW IT FITS

A ring of concrete 450 mm wide and 250 mm deep, top at ground level,
centred under the 305 mm wall. Outside 3,155 x 2,255 mm,
inside 2,255 x 1,355 mm. The setting-out plan gives every line.
Peg out the outside corners; check both diagonals are equal.
Dig the trench 450 wide and 250 deep; go deeper to firm ground if
the bottom is soft, and fill back with concrete, not soil.
Pour, rod out air, strike the top level all round within 5 mm.
Keep it damp under a sheet for 7 days before laying bricks.
Lay a plastic damp-proof strip 305 mm wide on top, under both
leaves and the cavity, lapped 150 mm at the joins.
Check: level within 5 mm all round; diagonals within 10 mm.

ZEERBOX

github.com/BoujeeEnjinia1701/zeerbox

ZeerBox wall strip footing: making sketch

DRAWING NO.	REV	SHEET	SIZE
ZBX-DWG-101	P1	1 of 1	ANSI B

SCALE	UNITS	PROJECTION	DATE	DRAWN
1:25	mm		2026-10-02	Amish Chadha

MATERIAL / NOTES

Concrete about 1 cement : 3 sand : 6 stone, about 1.0 m3

Licensed CERN-OHL-S-2.0 · Design Molecule Lab · designmolecule.com

Generated from cad/src; do not edit by hand