REV	DESCRIPTION	DATE	BY
P1	Making sketch for the prototype build plan	2026-10-02	AC

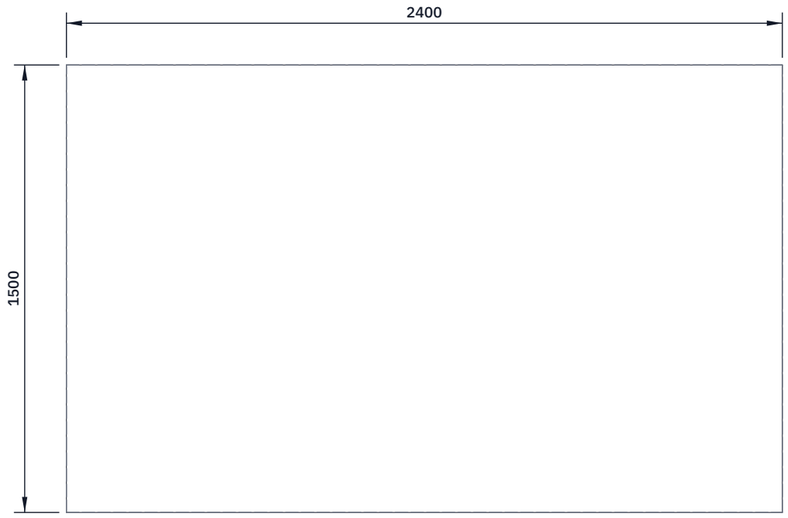

TOP VIEW

Scale 1:20; looking down (along -Z)

FRONT VIEW

Scale 1:20; looking at the front (along +Y)

RIGHT VIEW

Scale 1:20; looking at the right side (along -X)

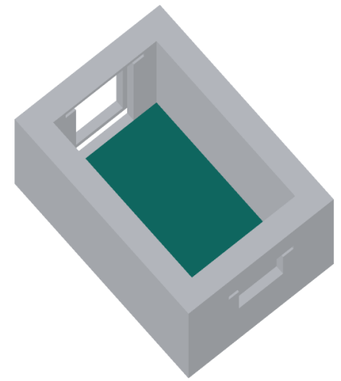

WHERE IT GOES

This part in colour, its neighbours in grey

HOW TO MAKE IT AND HOW IT FITS

Fills the room inside the inner leaf: 2,400 x 1,500 mm.
Level the ground inside the walls and compact it hard. Lay a 25 mm sand bed, screeded level.
Lay 75 mm bricks flat, close-jointed, in a stretcher bond; top 100 mm above ground, level with the door sill.
Brush dry sand into the joints and wet it down.
Check: level within 5 mm; no rocking brick.

ZEERBOX

github.com/BoujeeEnjinia1701/zeerbox

ZeerBox brick floor: making sketch

DRAWING NO.	REV	SHEET	SIZE
ZBX-DWG-105	P1	1 of 1	ANSI B

SCALE	UNITS	PROJECTION	DATE	DRAWN
1:20	mm		2026-10-02	Amish Chadha

MATERIAL / NOTES

Fired brick laid flat on a 25 mm sand bed

Licensed CERN-OHL-S-2.0 · Design Molecule Lab · designmolecule.com

Generated from cad/src; do not edit by hand