
CONCEPT, NOT FOR FABRICATION


ZeerBox · github.com/BoujeeEnjinia1701/zeerbox

REV	DESCRIPTION	DATE	BY
P2	Concept sheet	2026-10-24	AC

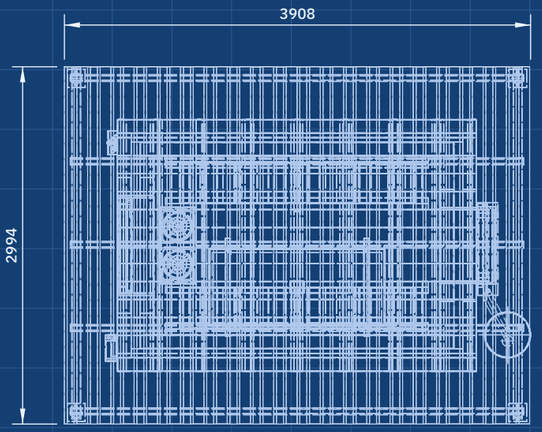


TOP VIEW

Scale 1:50; looking down (along -Z)

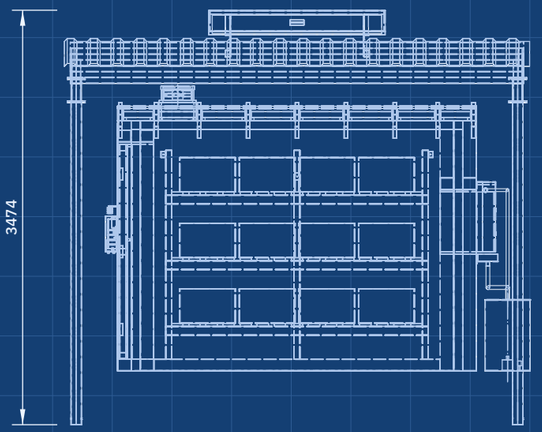


FRONT VIEW

Scale 1:50; looking at the front (along +Y)

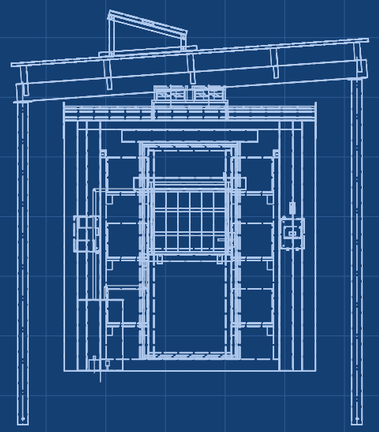

RIGHT VIEW

Scale 1:50; looking at the right side (along -X)

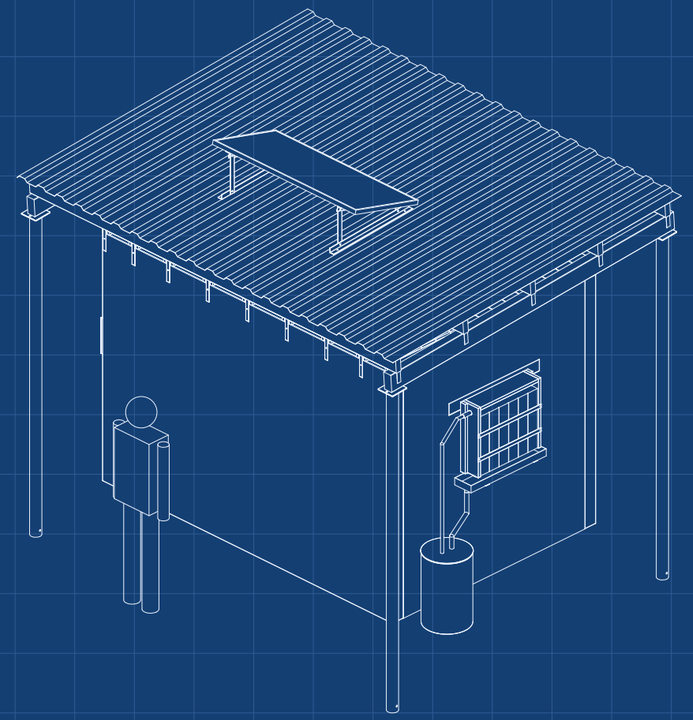

ISOMETRIC VIEW

Not to scale; grey is for scale; seen from the front right and above, about 30 deg elevation

KEY FIGURES

Room 2.4 x 1.5 x 2.0 m, 7.2 m3; 24 crates, 480 kg; top shelf 1.40 m
Design day 35 °C, 30 % RH: supply 23.1 °C, store 24.3 °C (ZBX-CAL-001)
About 560 m3/h through a 150 mm pad; store RH about 81 % (PR-003 80 %, at risk)
372 Wh/day from a 150 W panel (41 % margin); about 43 L water/day
Kit $300, value-engineering target $300; structure $574 separate (indicative)
Model detail D3: every part, fixing and weld (cad/fidelity.json)

ZEERBOX

github.com/BoujeeEnjinia1701/zeerbox

Walk-in evaporative store concept

DRAWING NO.	REV	SHEET	SIZE
ZBX-DWG-010	P2	1 of 1	ANSI B

SCALE	UNITS	PROJECTION	DATE	DRAWN
1:50	mm		2026-10-24	Amish Chadha

MATERIAL / NOTES

Massing model for concept communication

Licensed CERN-OHL-S-2.0 · Design Molecule Lab · designmolecule.com

Generated from cad/src; do not edit by hand