




CONCEPT, NOT FOR FABRICATION

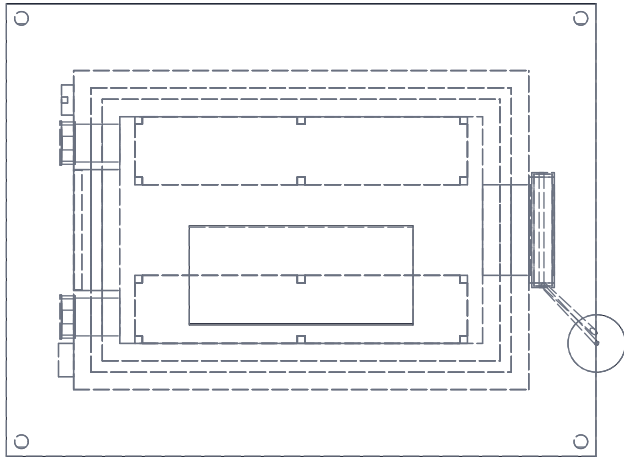


TOP VIEW
Scale 1:50

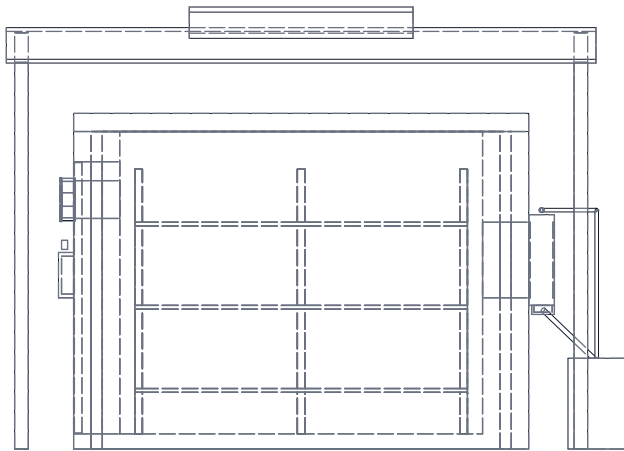

FRONT VIEW
Scale 1:50

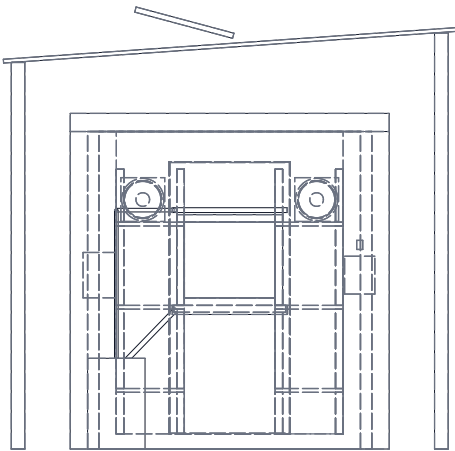

RIGHT VIEW
Scale 1:50

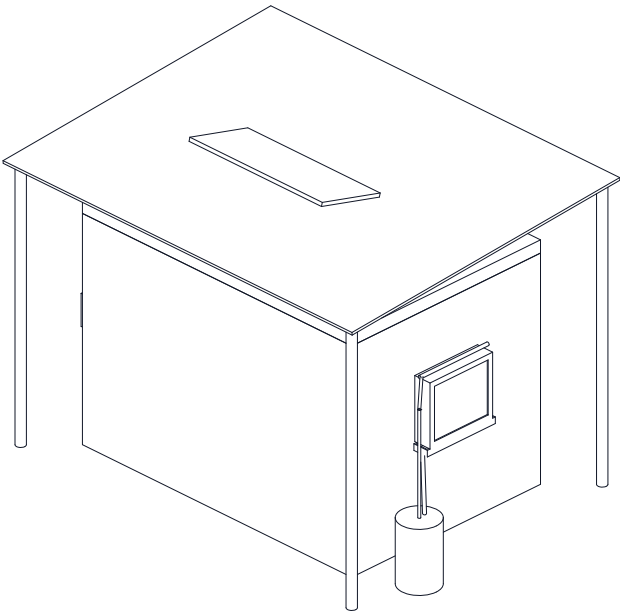

ISOMETRIC VIEW
Not to scale; crates hidden

KEY DIMENSIONS (MM) AND DATA

Overall 4095 x 2994 x 2924 H (roof, posts, sump, panel)
Room 2400 x 1500 x 2000 H inside; 7.2 m3
Walls 115 + 75 dry rice husk + 115 = 305; outside 3010 x 2110
Floor 100 brick on sand; wall top 2100; ceiling 120
Shade roof 3900 x 3000, 450 clear over ceiling, 4 deg
4 posts 90 dia, footings 500 sq x 600 deep
Door 800 x 1800, inside release, no outside lock
Pad 600 x 500 x 150, center 1250 above ground
2 fans 250 dia at 1650, 575 each side of door axis
Racks 2200 x 450; shelves 300, 850, 1400 above floor
Aisle 600; 24 crates; 150 W panel 1480 x 670
Design day: store 24.3 °C, 10.7 K drop, about 560 m3/h (CAL-001)
At risk at TRL 3: R3 (store RH 81 %, 77 % unfavorable, vs 80 %)
PRELIMINARY, NOT FOR FABRICATION

ZEERBOX

General arrangement, TRL 3 model

DRAWING NO. ZBX-DWG-001		REV P2	SHEET 1 of 1	SIZE ANSI B
SCALE 1:50	UNITS mm	PROJECTION 	DATE 2026-09-25	DRAWN Amish Chadha
MATERIAL / NOTES Fired brick, dry rice husk fill, timber, corrugated steel; 12 V kit. See bom/bom.csv				
Licensed CERN-OHL-S-2.0 · Design Molecule Lab · designmolecule.com				Generated from cad/src; do not edit by hand