



CONCEPT, NOT FOR FABRICATION

ZeerBox · github.com/BoujeeEnjinia1701/zeerbox

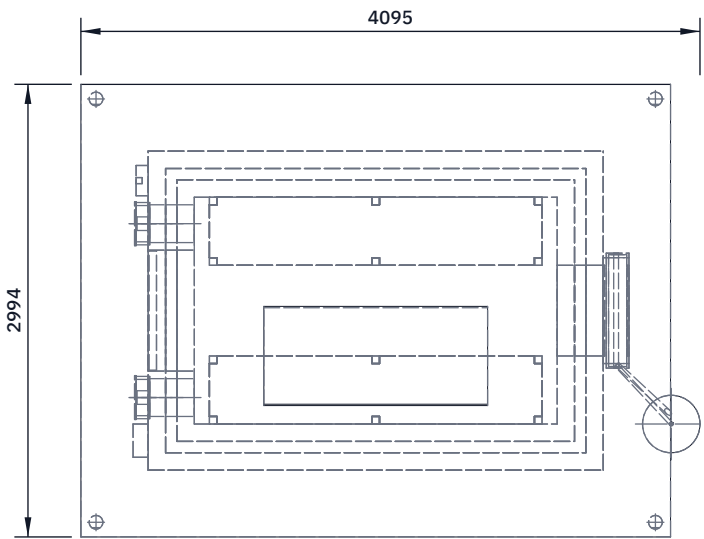


TOP VIEW

Scale 1:50; looking down (along -Z)

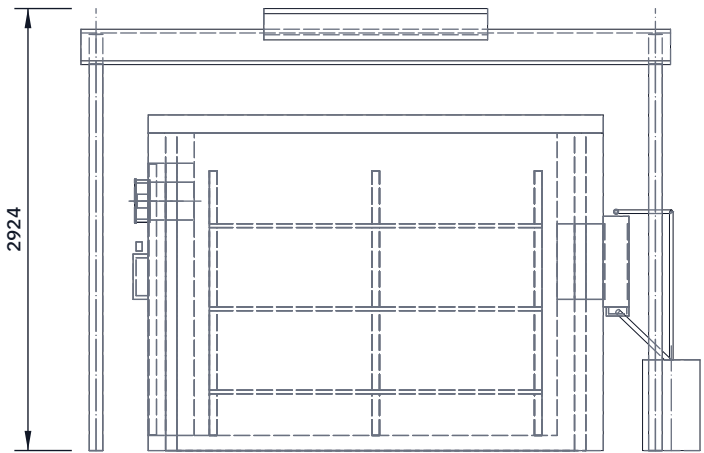


FRONT VIEW

Scale 1:50; looking at the front (along +Y)

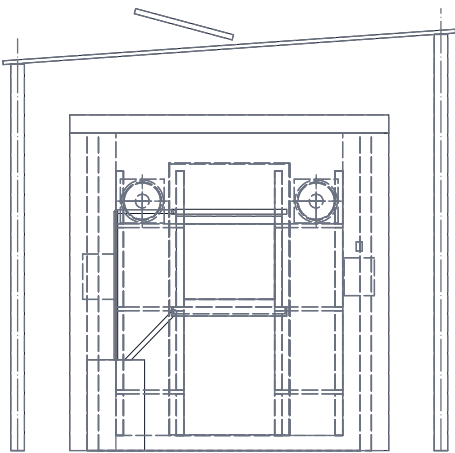

RIGHT VIEW

Scale 1:50; looking at the right side (along -X)

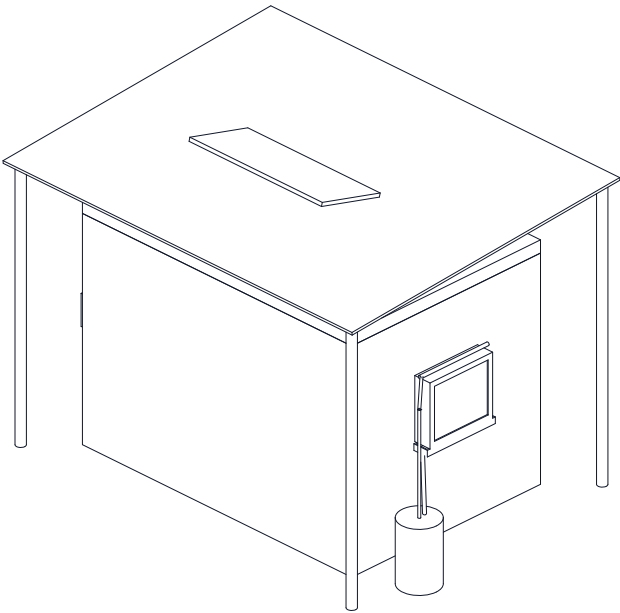

ISOMETRIC VIEW

Not to scale; crates hidden; seen from the front right and above, about 30 deg elevation

KEY DIMENSIONS (MM) AND DATA

Overall 4095 x 2994 x 2924 H (roof, posts, sump, panel)

Room 2400 x 1500 x 2000 H inside; 7.2 m³

Walls 115 + 75 dry rice husk + 115 = 305; outside 3010 x 2110

Floor 100 brick on sand; wall top 2100; ceiling 120

Shade roof 3900 x 3000, 450 clear over ceiling, 4 deg

4 posts 90 dia, footings 500 sq x 600 deep

Door 800 x 1800, inside release, no outside lock

Pad 600 x 500 x 150, center 1250 above ground

2 fans 250 dia at 1650, 575 each side of door axis

Racks 2200 x 450; shelves 300, 850, 1400 above floor

Aisle 600; 24 crates; 150 W panel 1480 x 670

Design day: store 24.3 °C, 10.7 K drop, about 560 m³/h (CAL-001)

At risk at TRL 3: R3 (store RH 81 %, 77 % unfavorable, vs 80 %)

PRELIMINARY, NOT FOR FABRICATION

ZEERBOX

github.com/BoujeeEnjinia1701/zeerbox

General arrangement, TRL 3 model

DRAWING NO. ZBX-DWG-001			REV P2	SHEET 1 of 1	SIZE ANSI B
SCALE 1:50	UNITS mm	PROJECTION 	DATE 2026-09-25		DRAWN Amish Chadha
MATERIAL / NOTES Fired brick, dry rice husk fill, timber, corrugated steel; 12 V kit. See bom/bom.csv					
Licensed CERN-OHL-S-2.0 · Design Molecule Lab · designmolecule.com				Generated from cad/src; do not edit by hand	