



CONCEPT, NOT FOR FABRICATION

ZeerBox · github.com/BoujeeEnjinia1701/zeerbox


REV	DESCRIPTION	DATE	BY
P1	Concept sheet	2026-09-26	AC

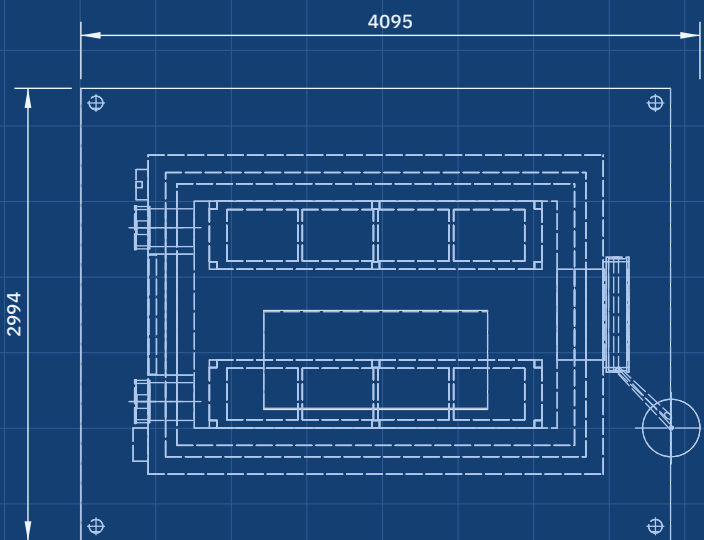


TOP VIEW
Scale 1:50; looking down (along -Z)

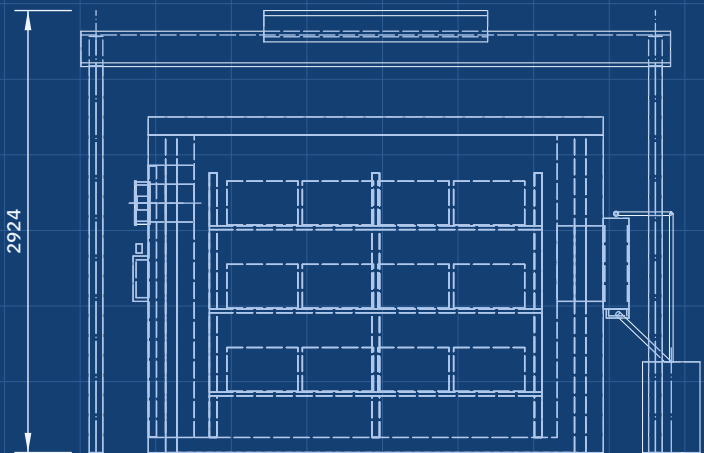

FRONT VIEW
Scale 1:50; looking at the front (along +Y)

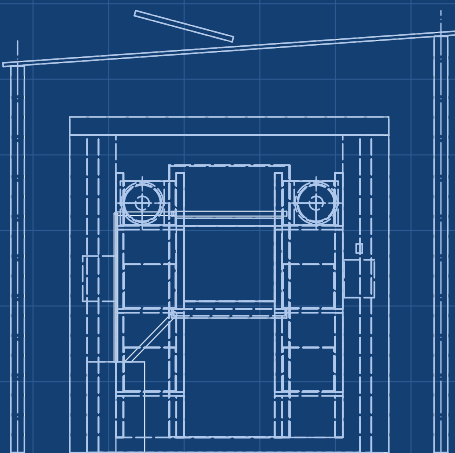

RIGHT VIEW
Scale 1:50; looking at the right side (along -X)

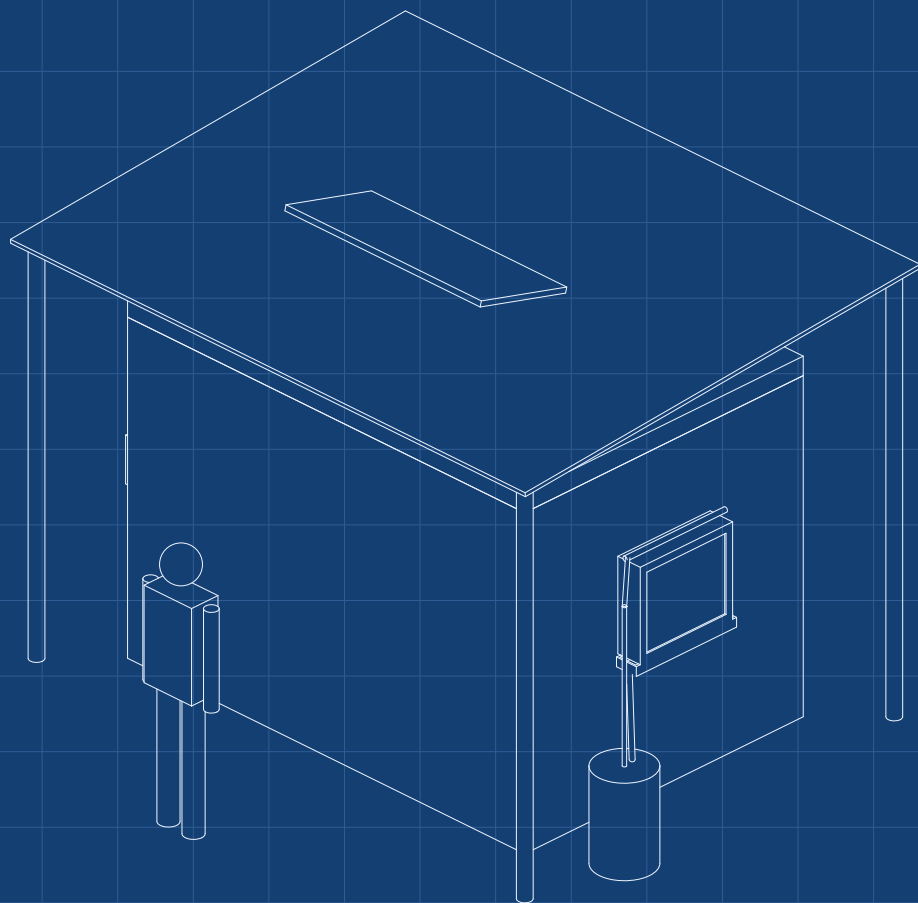

ISOMETRIC VIEW
Not to scale; grey is for scale; seen from the front right and above, about 30 deg elevation

KEY FIGURES

Room 2.4 x 1.5 x 2.0 m, 7.2 m³; 24 crates, 480 kg; top shelf 1.40 m
Design day 35 °C, 30 % RH: supply 23.1 °C, store 24.3 °C (ZBX-CAL-001)
About 560 m³/h through a 150 mm pad; store RH about 81 % (R3 80 %, at risk)
372 Wh/day from a 150 W panel (41 % margin); about 36 L water/day
Kit \$270 against \$300; structure \$355 costed separately (indicative)

ZEERBOX

github.com/BoujeeEnjinia1701/zeerbox

Walk-in evaporative store concept

DRAWING NO. ZBX-DWG-010		REV P1	SHEET 1 of 1	SIZE ANSI B
SCALE 1:50	UNITS mm	PROJECTION 	DATE 2026-09-26	DRAWN Amish Chadha
MATERIAL / NOTES Massing model for concept communication				
Licensed CERN-OHL-S-2.0 · Design Molecule Lab · designmolecule.com				Generated from cad/src; do not edit by hand