


REV	DESCRIPTION	DATE	BY
P1	Making sketch for the prototype build plan	2026-10-02	AC

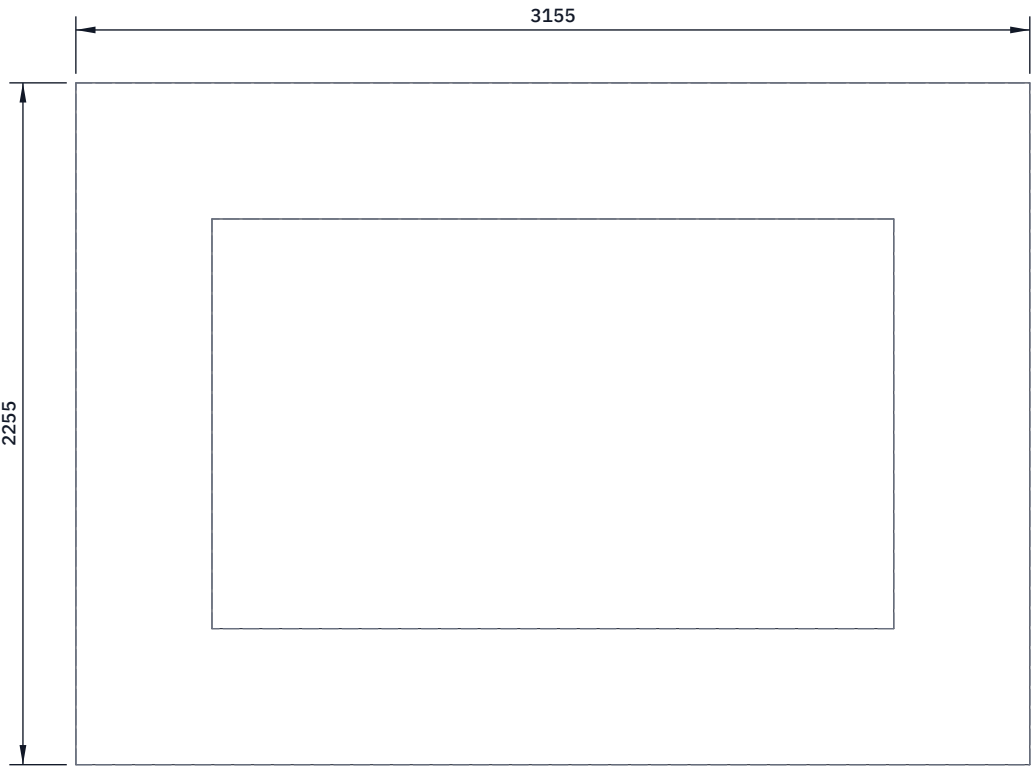

TOP VIEW

Scale 1:25; looking down (along -Z)




FRONT VIEW

Scale 1:25; looking at the front (along +Y)



RIGHT VIEW

Scale 1:25; looking at the right side (along -X)

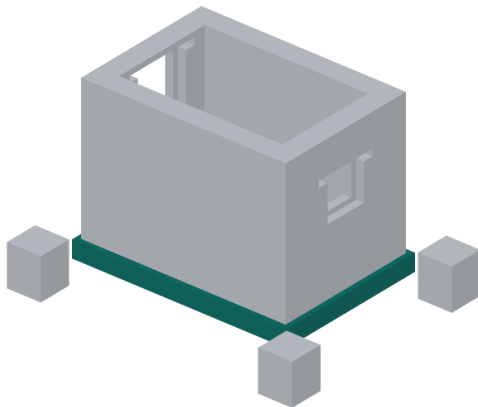

WHERE IT GOES

This part in colour, its neighbours in grey

HOW TO MAKE IT AND HOW IT FITS

A ring of concrete 450 mm wide and 250 mm deep, top at ground level, centred under the 305 mm wall. Outside 3,155 x 2,255 mm, inside 2,255 x 1,355 mm. The setting-out plan gives every line. Peg out the outside corners; check both diagonals are equal. Dig the trench 450 wide and 250 deep; go deeper to firm ground if the bottom is soft, and fill back with concrete, not soil. Pour, rod out air, strike the top level all round within 5 mm. Keep it damp under a sheet for 7 days before laying bricks. Lay a plastic damp-proof strip 305 mm wide on top, under both leaves and the cavity, lapped 150 mm at the joins. Check: level within 5 mm all round; diagonals within 10 mm.

ZEERBOX

github.com/BoujeeEnjinia1701/zeerbox

ZeerBox wall strip footing: making sketch

DRAWING NO. ZBX-DWG-101			REV P1	SHEET 1 of 1	SIZE ANSI B
SCALE 1:25	UNITS mm	PROJECTION 	DATE 2026-10-02		DRAWN Amish Chadha
MATERIAL / NOTES Concrete about 1 cement : 3 sand : 6 stone, about 1.0 m3					
Licensed CERN-OHL-S-2.0 · Design Molecule Lab · designmolecule.com				Generated from cad/src; do not edit by hand	