


REV	DESCRIPTION	DATE	BY
P1	Making sketch for the prototype build plan	2026-10-02	AC



TOP VIEW

Scale 1:10; looking down (along -Z)

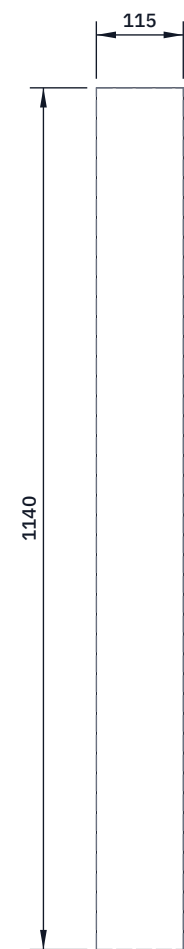


FRONT VIEW

Scale 1:10; looking at the front (along +Y)



RIGHT VIEW

Scale 1:10; looking at the right side (along -X)

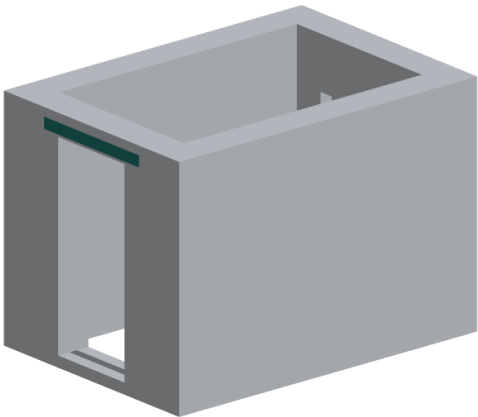

WHERE IT GOES

This part in colour, its neighbours in grey

HOW TO MAKE IT AND HOW IT FITS

Door lintels: two pieces 1,140 mm long, one over each leaf.

Pad lintels: two pieces 940 mm long, one over each leaf.

Section 115 wide (the leaf width) by 100 mm deep. Saw square, treat the cut ends again.

Each lintel bears 150 mm on the brick at both ends of the opening, bedded in mortar, level, flush with both leaf faces.

Door lintels: underside 1,920 mm above ground. Pad lintels: underside 1,520 mm.

Leave the cavity open between the two lintels of a pair; the fill above runs down between them onto the lining head.

Check: level, 150 mm bearing both ends, no rot or splits.

ZEERBOX

github.com/BoujeeEnjinia1701/zeerbox

ZeerBox lintels (make 4): making sketch

DRAWING NO. ZBX-DWG-104			REV P1	SHEET 1 of 1	SIZE ANSI B
SCALE 1:10	UNITS mm	PROJECTION 	DATE 2026-10-02		DRAWN Amish Chadha
MATERIAL / NOTES Termite-treated hardwood 115 x 100 mm					
Licensed CERN-OHL-S-2.0 · Design Molecule Lab · designmolecule.com					Generated from cad/src; do not edit by hand