


REV	DESCRIPTION	DATE	BY
P1	Making sketch for the prototype build plan	2026-10-02	AC

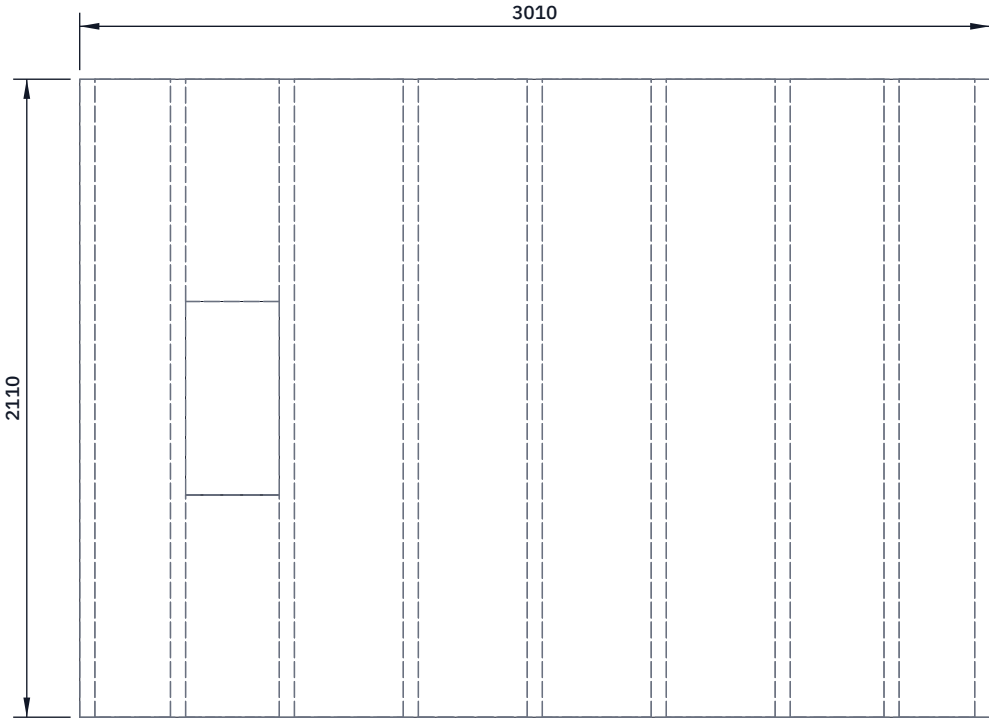

TOP VIEW

Scale 1:25; looking down (along -Z)




FRONT VIEW

Scale 1:25; looking at the front (along +Y)



RIGHT VIEW

Scale 1:25; looking at the right side (along -X)

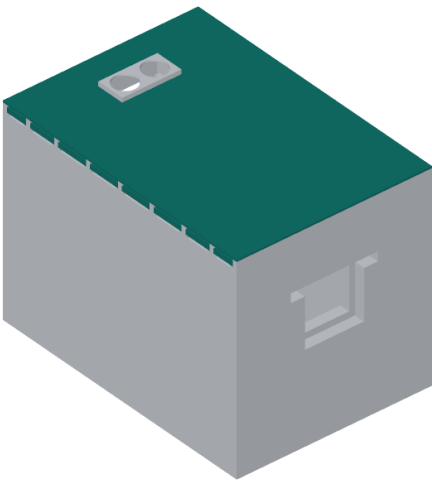

WHERE IT GOES

This part in colour, its neighbours in grey

HOW TO MAKE IT AND HOW IT FITS

Vapor sheet first: lay it over the cleats in each bay, lapped 100 mm up the joist sides.

Insulation: cut boards to fill each bay between joists, 2,110 mm long, resting on the cleats. Bays are 250 mm (ends), 310 mm (the fan bay, insulated outside the fan box only) and 360 mm.

Boards: 20 mm boards laid across the joists along the store, 3,010 x 2,110 mm in all, nailed to every joist.

Leave a 310 x 640 mm hole over the fan bay, 640 mm along the bay, centred across the store (the fan box comes up through it).

The boards are for occasional maintenance access only.

Check: no gaps between insulation boards; the fan hole is clear.

ZeerBox ceiling insulation and boards: making sketch

DRAWING NO. ZBX-DWG-109			REV P1	SHEET 1 of 1	SIZE ANSI B
SCALE 1:25	UNITS mm	PROJECTION 	DATE 2026-10-02		DRAWN Amish Chadha
MATERIAL / NOTES 50 mm straw board or foam board; plastic vapor sheet; 20 mm boards					
Licensed CERN-OHL-S-2.0 · Design Molecule Lab · designmolecule.com				Generated from cad/src; do not edit by hand	