


REV	DESCRIPTION	DATE	BY
P1	Making sketch for the prototype build plan	2026-10-02	AC

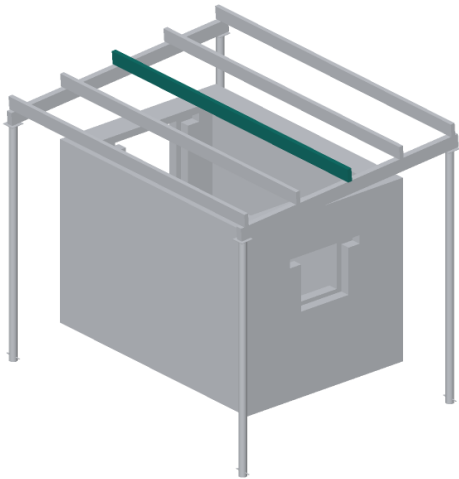


WHERE IT GOES

This part in colour, its neighbours in grey

HOW TO MAKE IT AND HOW IT FITS

Cut five 3,800 mm lengths of 50 x 150 mm; treat the ends.
Each lies on edge across both beams along the store, at the marks
700 mm apart, ends 12 mm past the beams' outer faces.
Fix each crossing with a galvanized hurricane tie rated 2 kN or
more, nailed with the tie maker's nails (the wind lifts about
1.1 kN at each crossing, ZBX-CAL-001 section 10).
A 100 mm deep purlin is not strong enough for this span.
Check: tops in one plane within 5 mm (string line across).

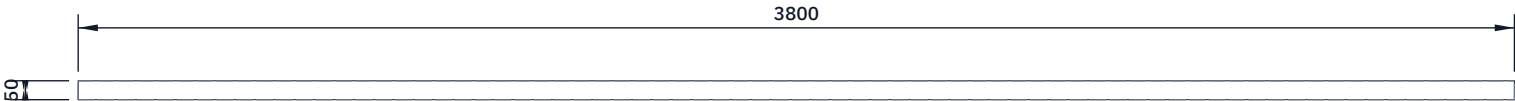

TOP VIEW

Scale 1:20; looking down (along -Z)



FRONT VIEW

Scale 1:20; looking at the front (along +Y)



RIGHT VIEW

Scale 1:20; looking at the right side (along -X)

ZEERBOX

github.com/BoujeeEnjinia1701/zeerbox

ZeerBox purlin (make 5): making sketch

DRAWING NO. ZBX-DWG-112			REV P1	SHEET 1 of 1	SIZE ANSI B
SCALE 1:20	UNITS mm	PROJECTION 	DATE 2026-10-02		DRAWN Amish Chadha
MATERIAL / NOTES Sawn timber 50 x 150 mm, treated; hurricane ties					
Licensed CERN-OHL-S-2.0 · Design Molecule Lab · designmolecule.com				Generated from cad/src; do not edit by hand	